
Földszinti alaprajz, m=1:100

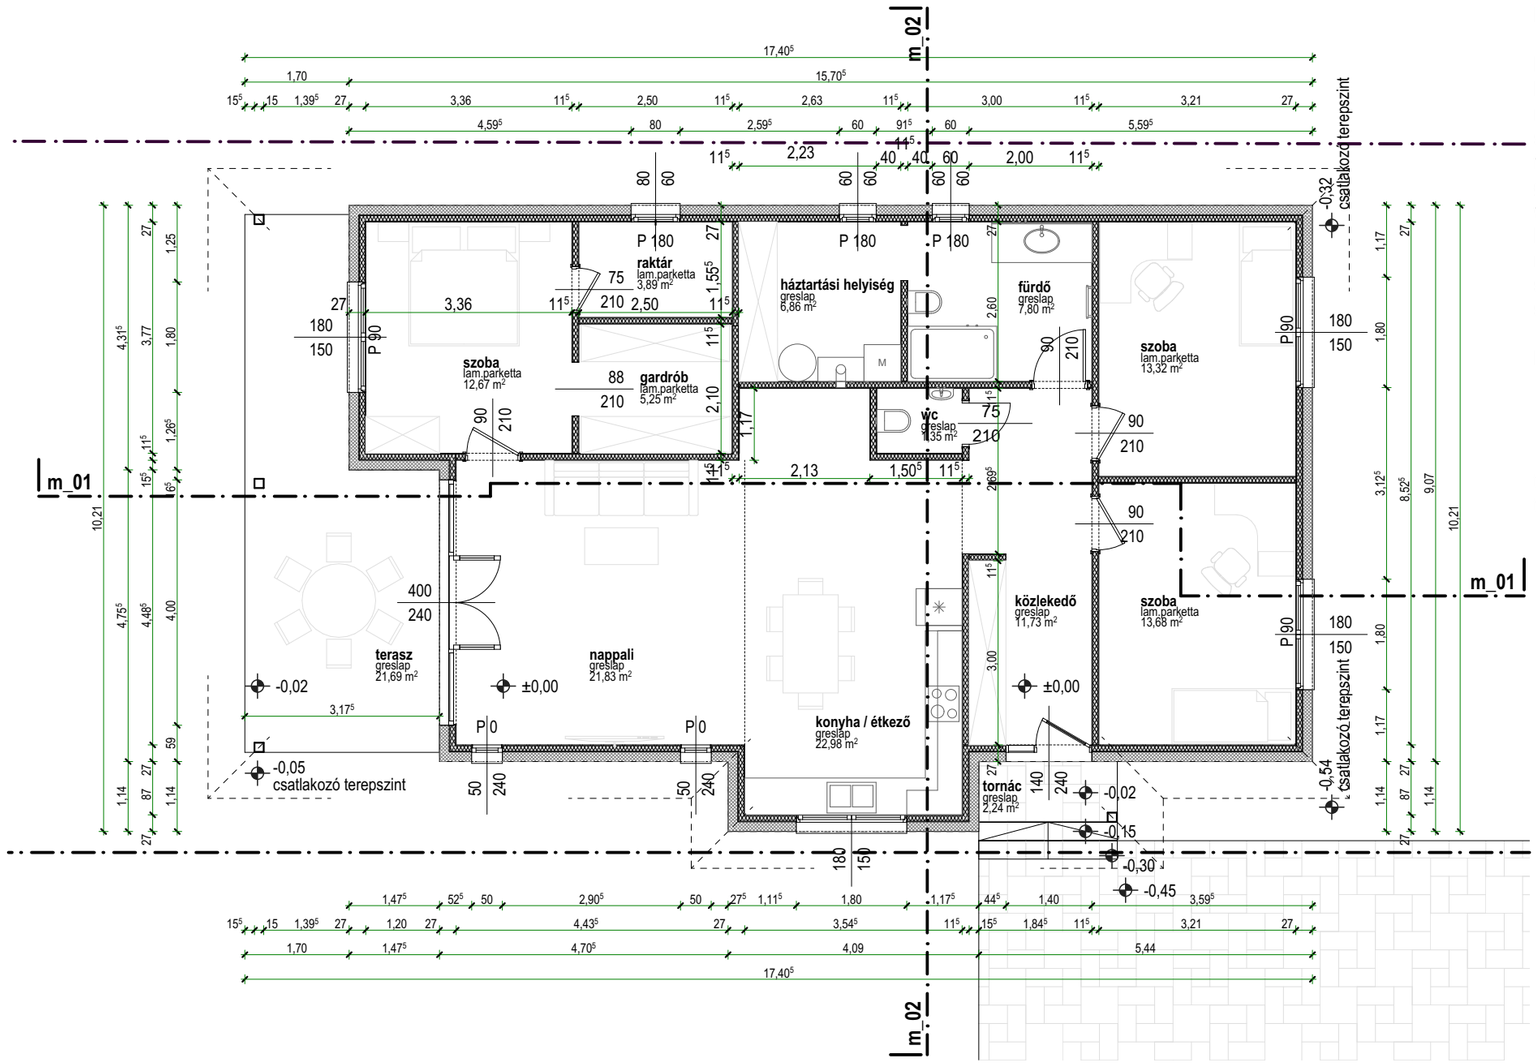

helyiséglista	burkolat	hasznos alapterület
közlekedő	greslap	11,73 m2
konyha, étkező	greslap	22,98 m2
nappali	greslap	21,83 m2
szoba	lam_parketta	12,67 m2
fürdő	greslap	7,80 m2
gardrób	lam_parketta	5,25 m2
wc	greslap	1,35 m2
háztartási helyiség	greslap	6,86 m2
raktár	lam_parketta	3,89 m2
szoba	lam_parketta	13,32 m2
szoba	lam_parketta	13,68m2
lakás hasznos alapterület		**121,36 m2**
tornác	greslap	2,24 m2
terasz	greslap	21,69 m2

Tervezés tárgya
Családi ház tervezése

Terv fajtája
Egyszerű bejelentési tervdokumentáció

Építés helye, helyrajzi száma
2028 Pilismarót, Esztergomi út 83,
hrsz: 769/1

Megbízó neve, címe
Szluha-Juhász Renáta
és Szluha Bálint Pál
2509 Esztergom, Blaha Lujza utca 2.

Dátum
2022. január hó

Tervlap száma
É-01

Felelős tervező
Schön Csaba
okleveles építészmérnök
É 11-0346
info@viarstudio.hu
+3670/3152116

Tervező munkatárs
Takács Petra Renáta
okleveles építészmérnök
takacs.petra.renata@gmail.com
+3670/3217276

VIAR STUDIO

Ez a terv szerzői jogi oltalom alá esik. A Megbízónak az átadott tervet mind egészében, mind részleteiben egyszeri alkalommal van joga felhasználni. Harmadik személynek csak a Tervező írásos hozzájárulásával adhatja át.